Détail menuiserie 1/20 : voir pièce 4

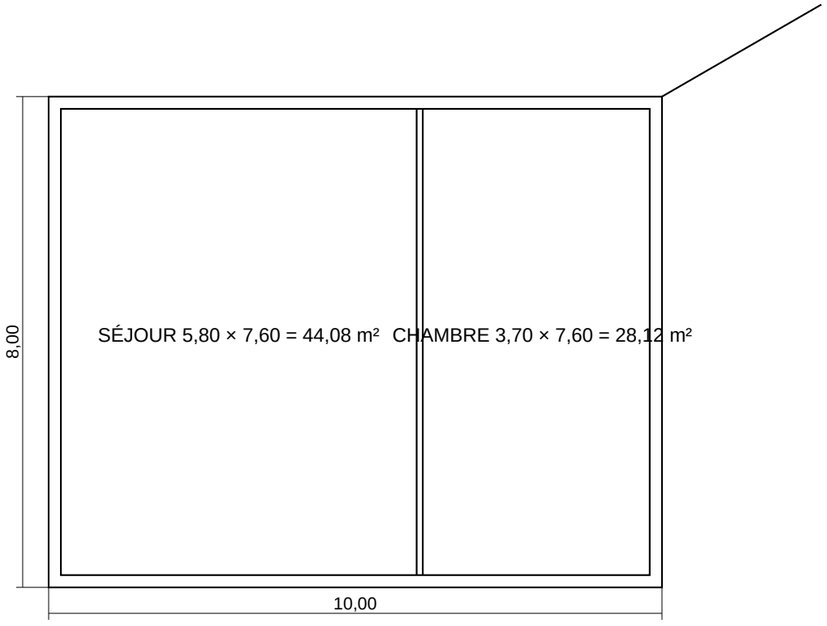

PLAN RDC (page exacte)
Échelle : 1/100
Indice B — 12/03/2026 — Lot 1/3

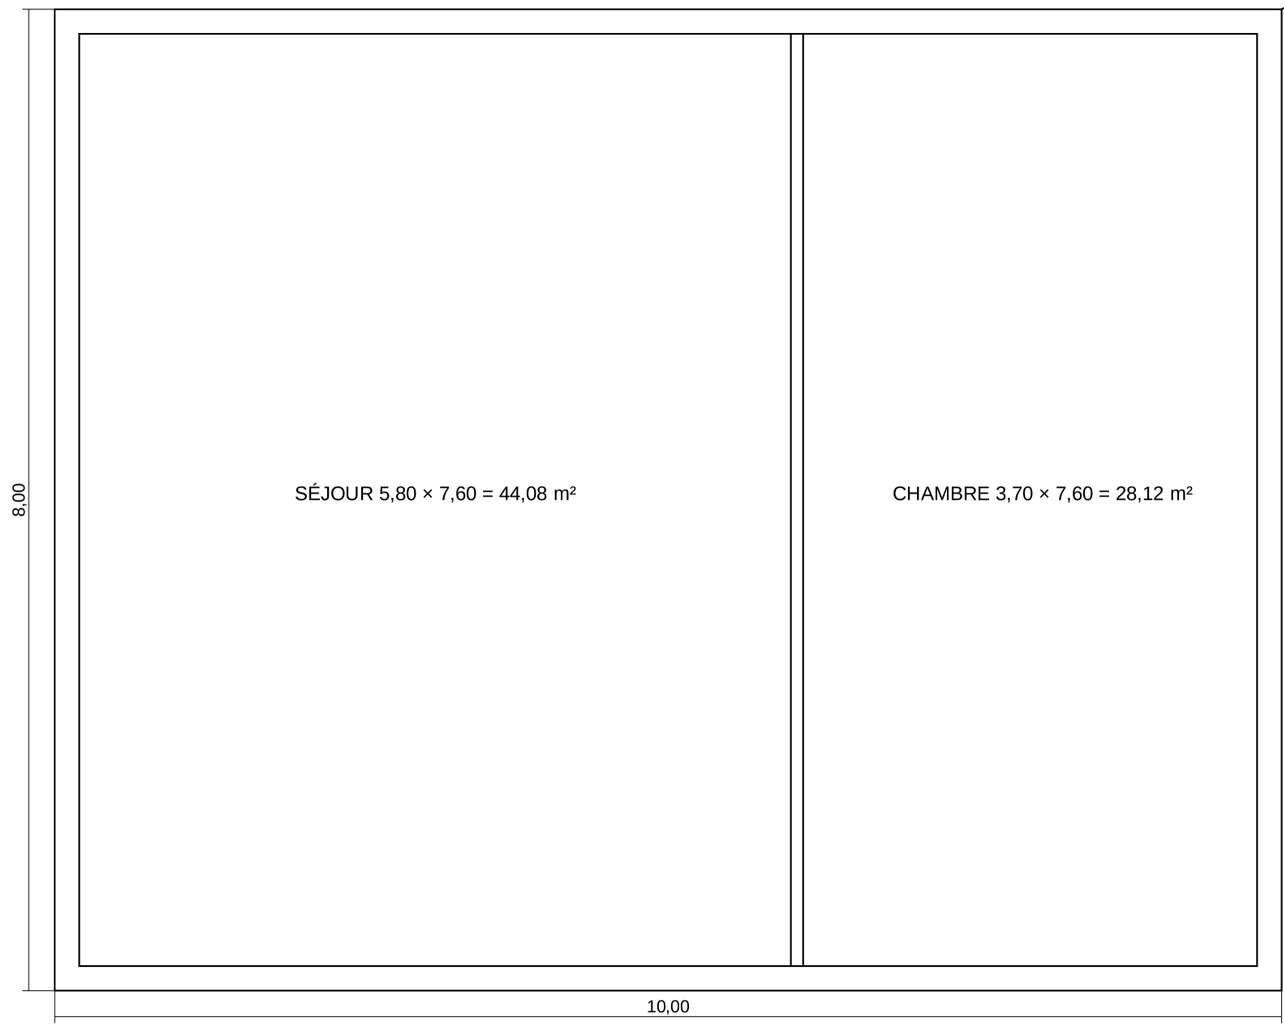
SÉJOUR 5,80 × 7,60 = 44,08 m²
CHAMBRE 3,70 × 7,60 = 28,12 m²
8,00
10,00

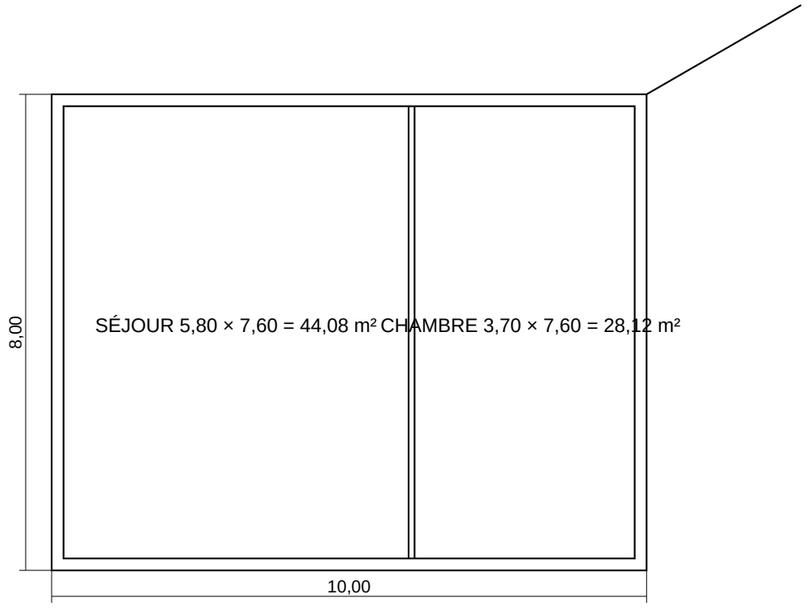

PLAN RDC (imprimé à 97 %)

Échelle : 1/100

Indice B — 12/03/2026 — Lot 1/3